

All rights reserved. Passing on and copying of this document, use and communication of its contents not permitted without written authorization.
© 2026 HITACHI Rail Austria

Jede Vervielfältigung, Weitergabe des Inhaltes oder sonstige Verwertung darf nur mit schriftlicher Ermächtigung erfolgen.
© 2026 HITACHI Rail Austria


Minden jog fenntartva. A jelen dokumentum átadása és másolása, valamint tartalmának felhasználása és közlése írásos meghatalmazás nélkül tilos.
© 2026 HITACHI Rail Austria

Construction of the Zalaszentiván Delta track GYŐR - SOPRON - EBENFURT RAILWAY


Változások / Changes:

Ed. 01PD01 – 2026.08.17
Első kiadás / First Edition

Ed. 01PD02 – 2026.09.04
Véleményezett 01PD01 verzió / Reviewed version 01PD01

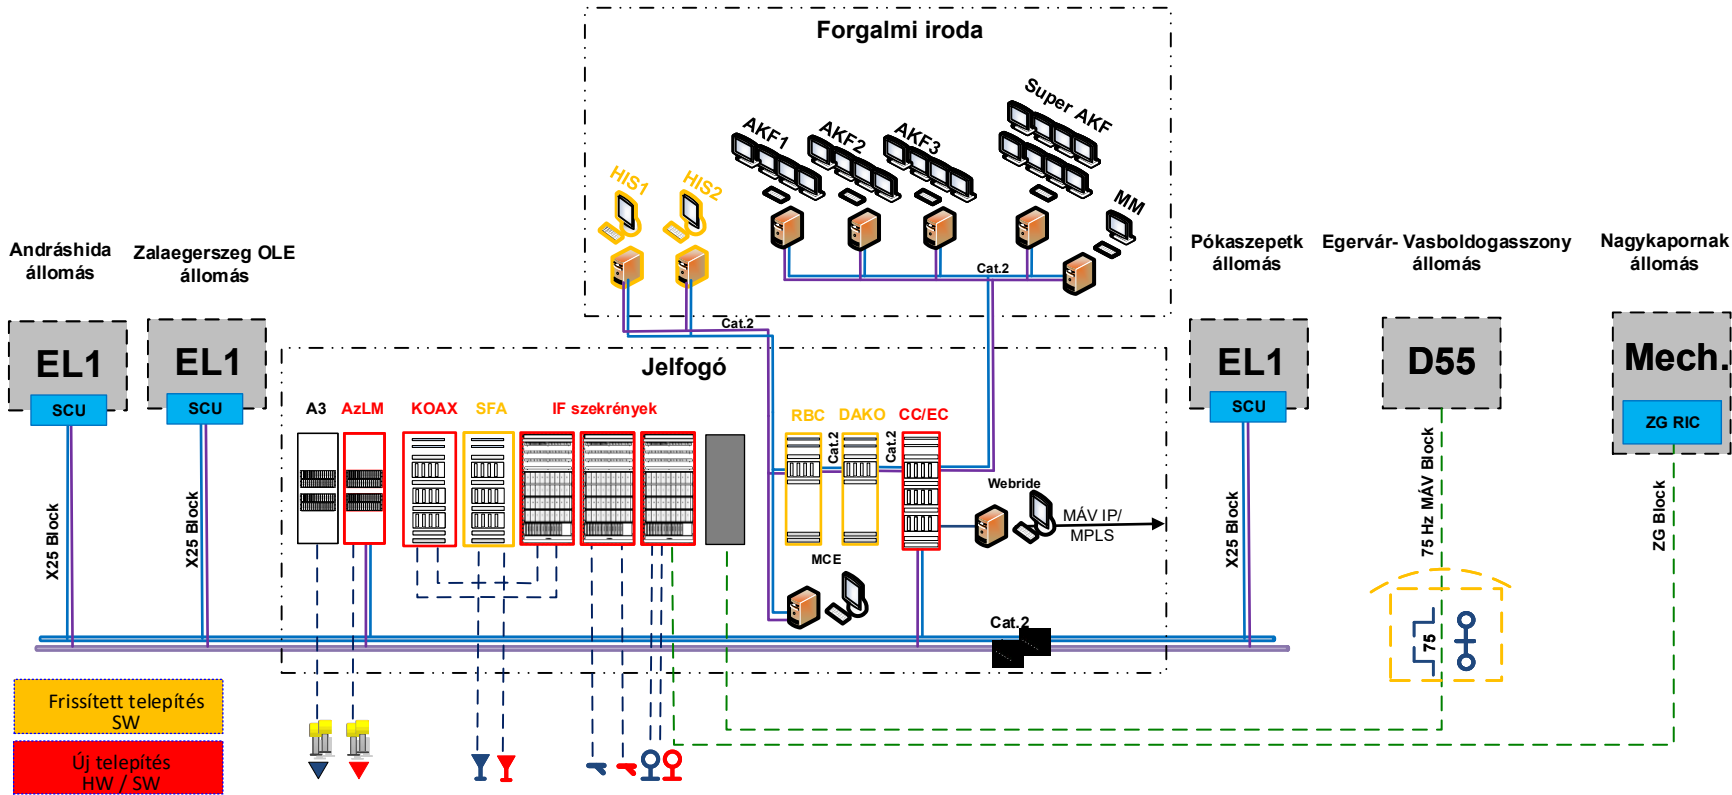

Jelmagyarázat - Legend:

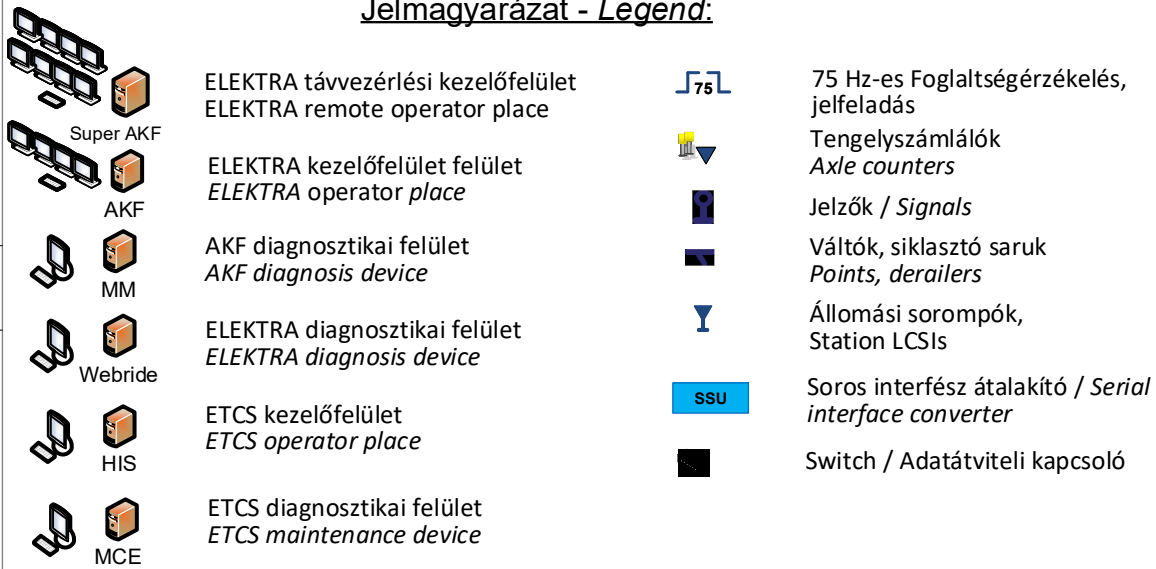

Comments / Megjegyzés:

Category 1 and 2 networks are connected between locations.

Kategória 1 és 2-es hálózatok össze vannak kötve a helyszínek között.

FO connection between stations include double redundant rings on cables with separated routes.

Optikai kábeles összeköttetések az Állomások között dupla redundáns gyűrűben vannak, A kábelek eltérő nyomvonalon futnak.

Projekt / Project: Zalaszentiván Delta vágány építése GYŐR - SOPRON - EBENFURT VASÚT/ Construction of the Zalaszentiván Y track GYŐR - SOPRON - EBENFURT RAILWAY				
Terv / Plan: Előterv / Preliminary Plan				
Rajz / Drawing: Biztosítóberendezési rendszervázlat / Interlocking system architecture				
Rajzsám / Drawing no.: 3BU 61914 0016 PEAPQ		Verzió / Version: ED 01PD02	Dátum / Date: 2026.08.17	Oldal / Page: 1/1
Szerkesztő / Editor: S.Németh		Jóváhagyta / Approved by: R. Szalay		
Vállalat / Company: HITACHI RAIL Austria GmbH		Üzemeltető / Operator: GYSEV Zrt.		
Vállalkozó / Contractor: HITACHI				